


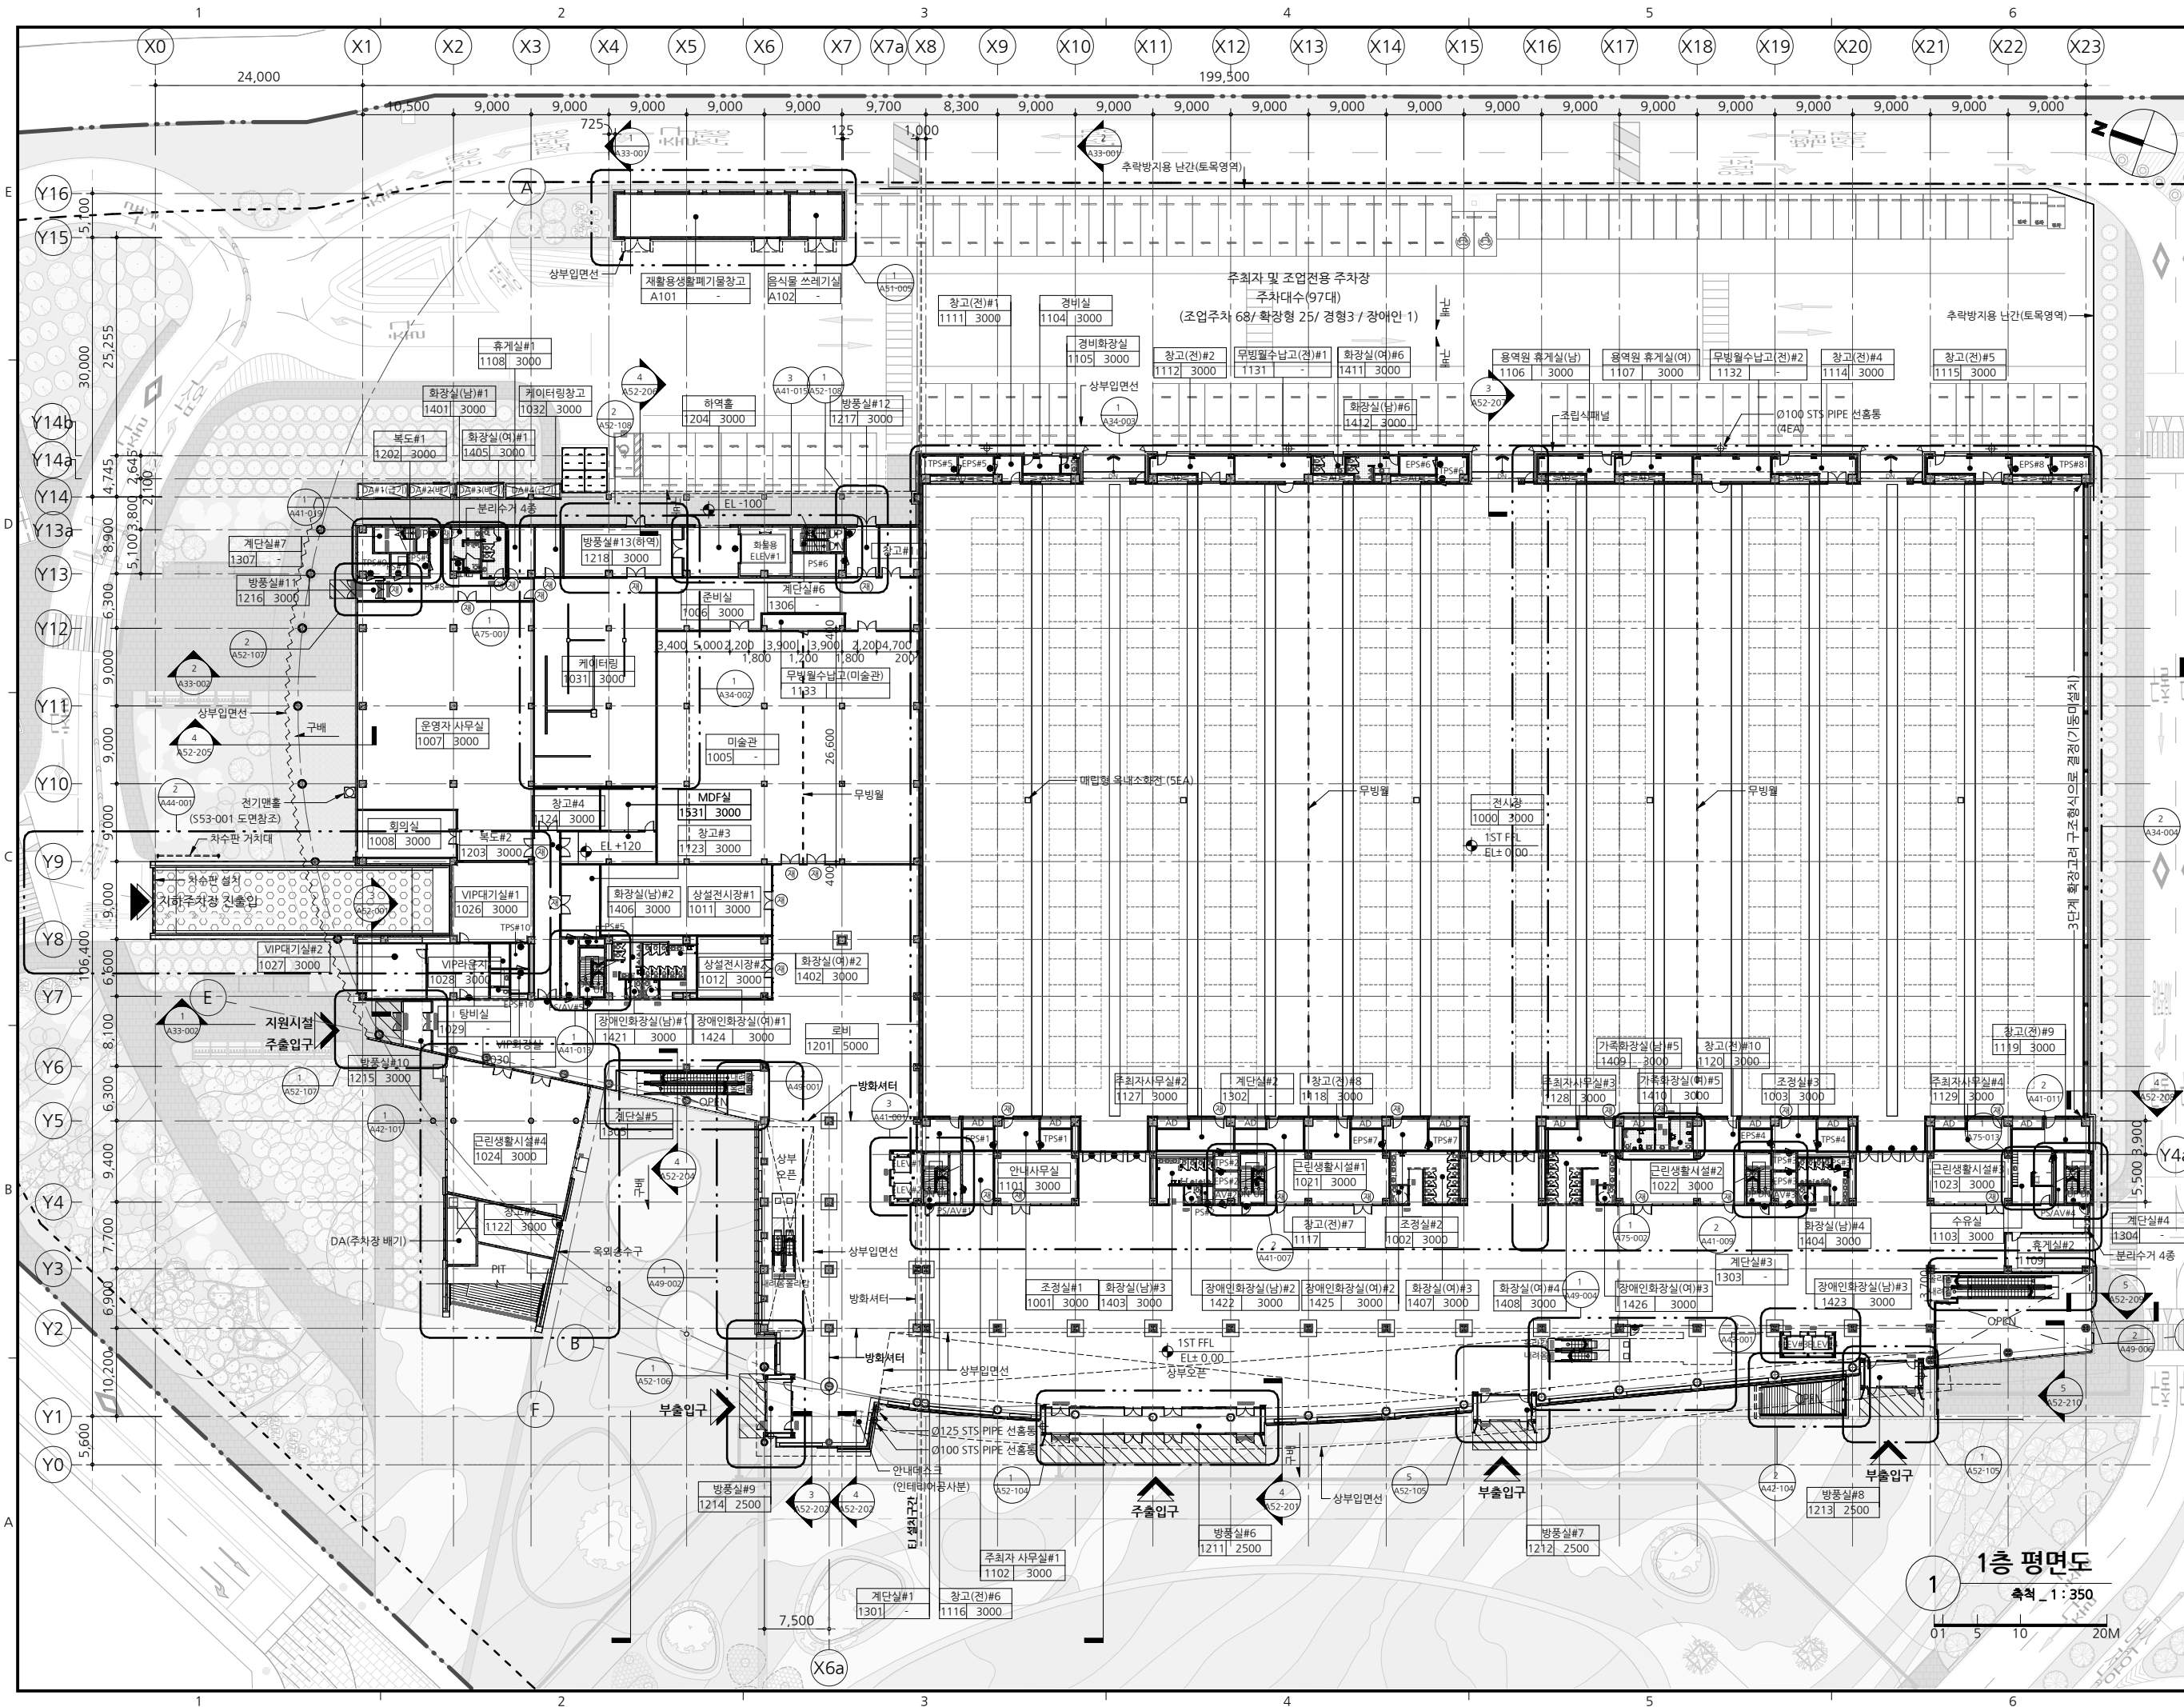

- NOTE
- 본 건축물 1층 바닥 마감 레벨(1ST FFL)인 EL±0.00은 토목측량표고 31.20 M임.
 - 표기는 강중방화문, 방화승강기문임.
 - ▲ 표기는 소방진압장치임.
 - ◎ : 재료분리대 ⊕ : 옥내소화전 ⊖ : 방수기구함
 - 설비관련 개구부는 설비 담당자와 위치 및 크기를 협의하여 공사감독자의 승인을 득한 후 시공할 것.
 - 인테리어 부분 시공시 벽체, 천장, 문, 계단, 난간 등의 관계법령 적합성 및 구조안전성을 별도로 확인하여 공사감독자의 승인을 득한 후 시공할 것.
 - 장애인을 위한 ELEV 호출버튼 30cm 전면에 경향블록 설치할 것.
 - 상기 NOTE 외에 도면 작성 및 시공 기준은 건축일반방사를 참조할 것.
 - 인테리어 공사, 입주자 공사 등 별도공사는 해당 도면 참조할 것.
 - 무빙월 시공 시 전문업체의 시공상태도를 작성하여 공사감독자의 승인을 득한 후 시공할 것.
 - 옥내의 소화전 설치 전 관련공종 협의 후 SHOP DWG 작성하고 감독관의 승인을 득하여 시공할 것.
 - 전시장 내 옥내소화전 위치는 소방서 협의하고 관련 허가부서 협의 후 SHOP DWG 작성하고 설계자, 발주처 및 공사감독자의 승인을 득한 후 시공할 것.
 - ▨ = 평지구간



20	20	20
20	20	20
20	20	20
수정번호	수정내용	
작성일자	검토일자	승인일자
작성인	검토인	승인인



1주1매안건축
서울특별시 강남구 테헤란로 200 해안빌딩, 06135
T: 82 2 3438 8000 F: 82 2 3438 8100 www.haeahn.com

(주)라온 건축사사무소
충북 청주시 흥덕구 서현서로 29, 4층
TEL : 043 235 4778 FAX : 043 235 4779

프로젝트명
충북청주전시장 건립사업
건축실시시설계용역

도면명
1층 평면도

축척
A1 : 1/350 | A3 : 1/700

PJ CODE	작성	검토	승인
20184	이찬주	이병술	오현석

도면번호
A31-002